

MÉRETSPECIFIKÁCIÓ

Ajánlat sz.280kelt2026-01-29 10:15

Vonatkozás

TetőHáz 1Elhelyezkedés

Pozíció leírása								Mennyisé g	Mértéke gység
-----------------	--	--	--	--	--	--	--	---------------	------------------

BONA PLUS 2.0 350								263,59	m2
-------------------	--	--	--	--	--	--	--	--------	----

#1	5560	4	26,51	#16	2780	4	13,26
#2	5450	1	6,50	#17	2600	2	6,20
#3	5180	2	12,35	#18	2590	2	6,17
#4	4950	2	11,80	#19	2360	2	5,63
#5	4170	4	19,88	#20	2200	2	5,24
#6	3890	2	9,27	#21	2030	1	2,42
#7	3880	2	9,25	#22	1870	1	2,23
#8	3650	2	8,70	#23	1390	4	6,63
#9	3530	9	37,87	#24	1300	4	6,20
#10	3500	2	8,34	#25	1150	2	2,74
#11	3450	4	16,45	#26	1100	1	1,31
#12	3350	3	11,98	#27	1060	2	2,53
#13	3180	2	7,58	#28	930	1	1,11
#14	3090	2	7,37	#29	450	1	0,54
#15	2970	2	7,08	#30	380	1	0,45

Összefoglalás 73

TetőHáz 2Elhelyezkedés

Pozíció leírása								Mennyisé g	Mértéke gység
-----------------	--	--	--	--	--	--	--	---------------	------------------

BONA PLUS 2.0 350								70,8	m2
-------------------	--	--	--	--	--	--	--	------	----

#1	3600	3	12,87
#2	2700	18	57,93

Összefoglalás 21

TetőHáz 3Elhelyezkedés

Pozíció leírása								Mennyisé g	Mértéke gység
-----------------	--	--	--	--	--	--	--	---------------	------------------

BONA PLUS 2.0 350								88,57	m2
-------------------	--	--	--	--	--	--	--	-------	----


#1	3200	12	45,77
#2	3100	2	7,39
#3	2710	2	6,46
#4	2590	2	6,17
#5	2420	4	11,54
#6	1360	2	3,24
#7	1230	2	2,93
#8	1060	4	5,05

Összefoglalás 30

Szerelési útmutató

Tető	Ház 1	Felület	41,65m ² (Σ=200,32m ²)	Dőlésszöge	0,0
Felület	Utcafront	Körfogat	30,27m		

Anyag	BONA PLUS 2.0 350	Mennyiség	53,38 m2	Utcafront	ΔX: 0	ΔY:
-------	-------------------	-----------	----------	-----------	-------	-----

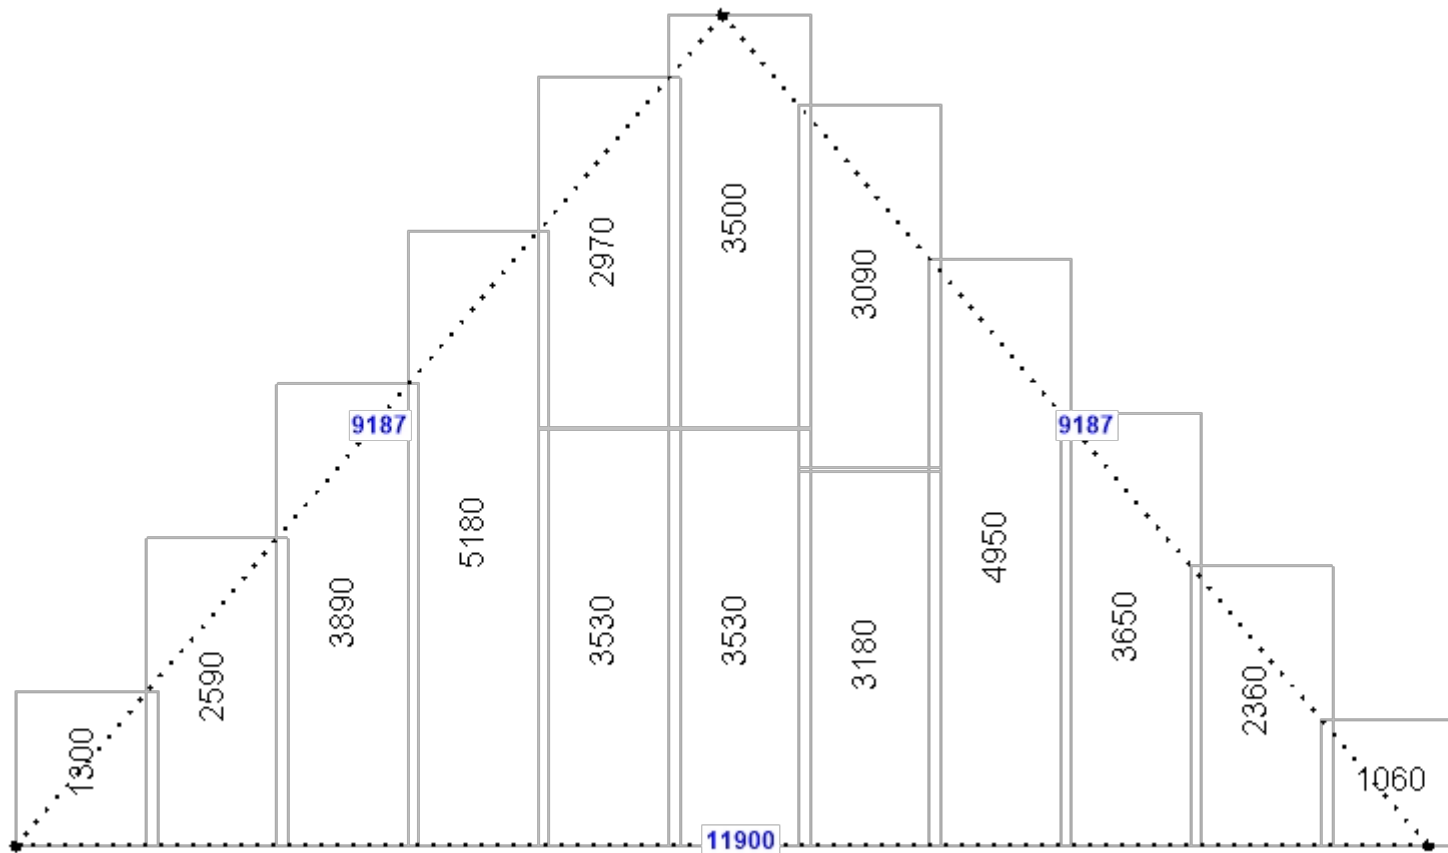


Length | Number of sheets | Area E | Area T

Szerelési útmutató

Tető	Ház 1	Felület	41,65m ² (Σ=200,32m ²)	Dőlésszöge	0,0
Felület	Utcafront tükörképe	Körfogat	30,27m		

Anyag	BONA PLUS 2.0 350	Mennyiség	53,38 m2	Utcafront tükörképe	ΔX: 0	ΔY:
-------	-------------------	-----------	----------	---------------------	-------	-----

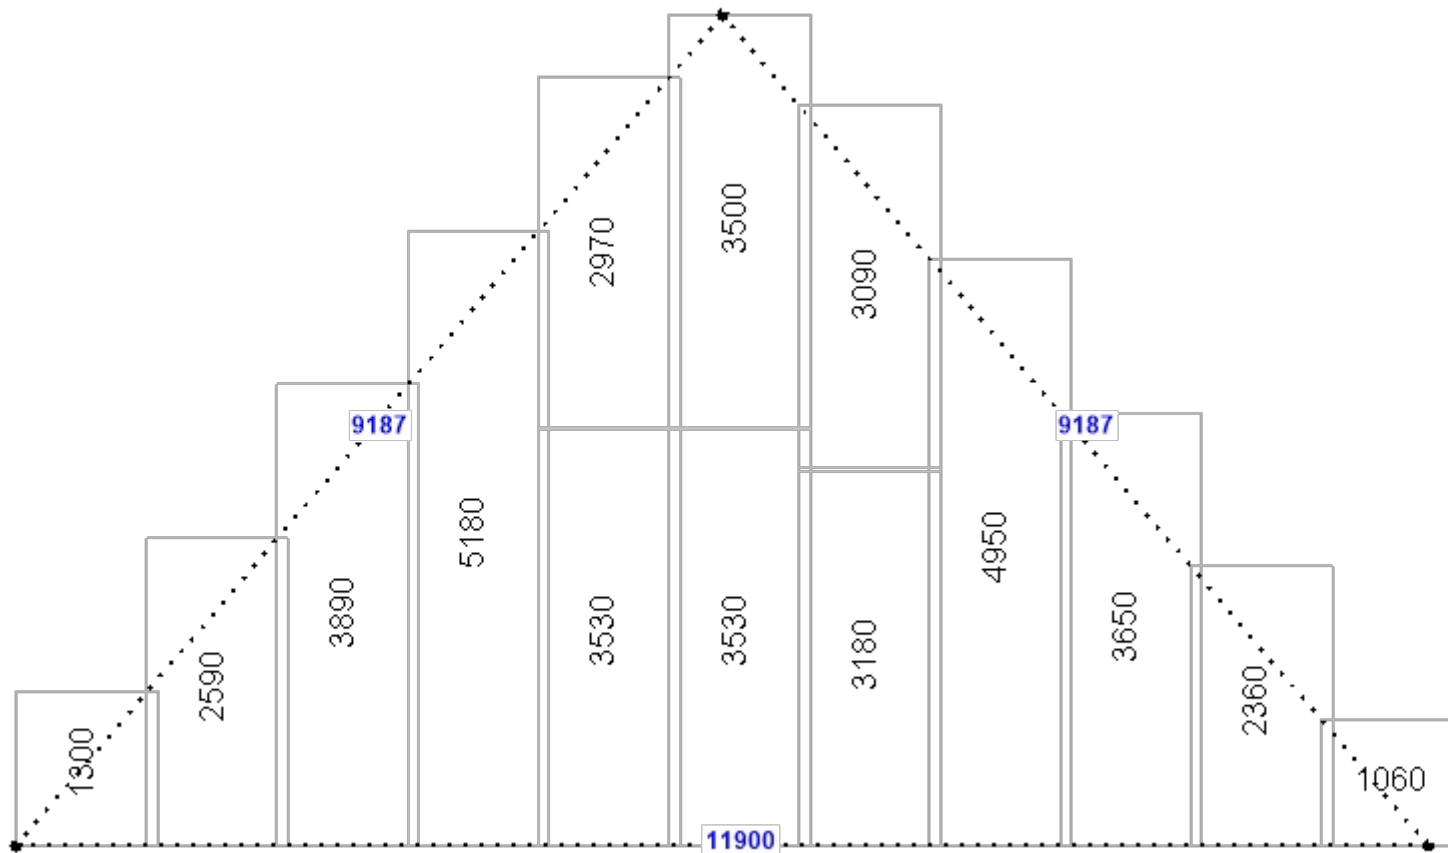


Length | Number of sheets | Area E | Area T

Szerelési útmutató

Tető	Ház 1	Felület	54m ² (Σ=200,32m ²)	Dőlésszöge
Felület	Szomszéd felőli oldal	Körfogat	33,37m	

Anyag	BONA PLUS 2.0 350	Mennyiség	67,01 m2	Szomszéd felőli oldal	ΔX: 0	ΔY:
-------	-------------------	-----------	----------	-----------------------	-------	-----

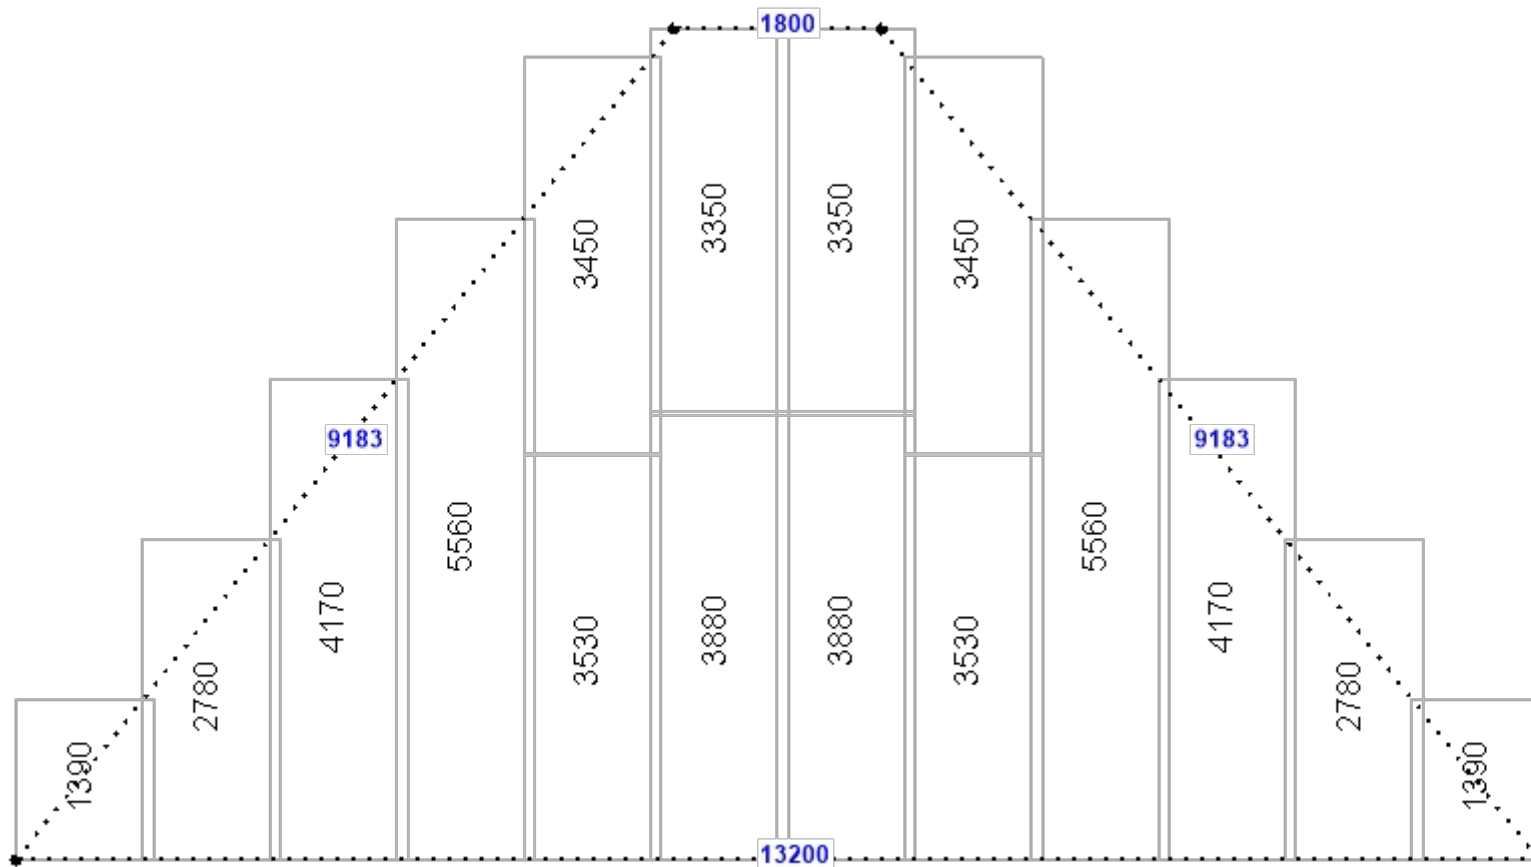


Length | Number of sheets | Area E | Area T

Szerelési útmutató

Tető	Ház 1	Felület	48,5m ² (Σ=200,32m ²)	Dőlésszöge
Felület	Udvar	Körfogat	36,17m	

Anyag	BONA PLUS 2.0 350	Mennyiség	64,48 m2	Udvar	ΔX: 0	ΔY:
-------	-------------------	-----------	----------	-------	-------	-----

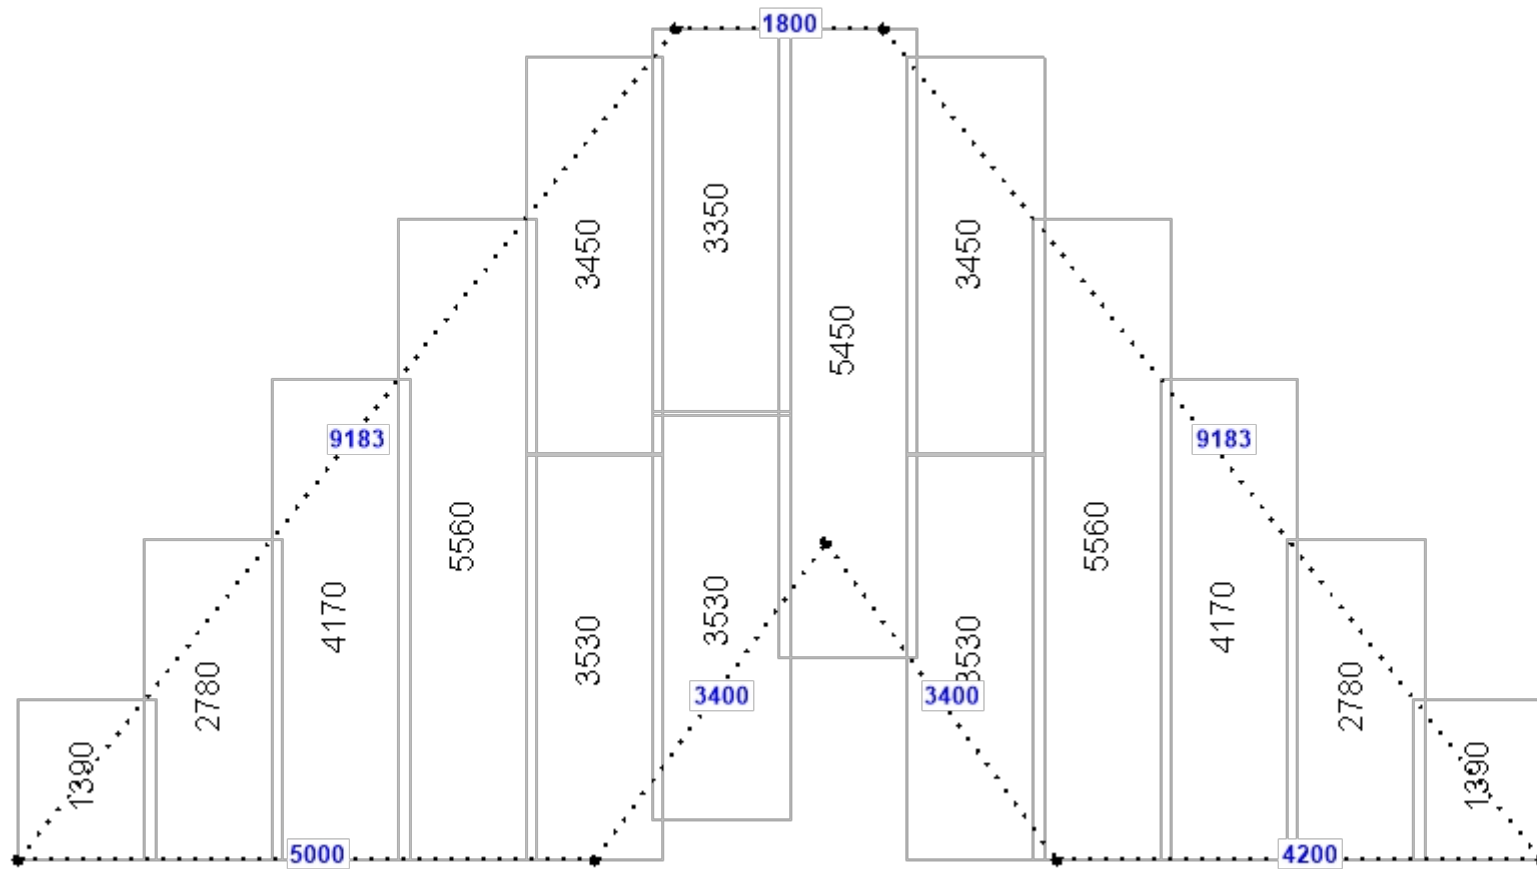


Length | Number of sheets | Area E | Area T

Szerelési útmutató

Tető	Ház 1	Felület	4,4m ² (Σ=200,32m ²)	Dőlésszöge
Felület	Udvar kiugró 1	Körfogat	10,81m	

Anyag	BONA PLUS 2.0 350	Mennyiség	8,18 m2	Udvar kiugró 1	ΔX: 0	ΔY:
-------	-------------------	-----------	---------	----------------	-------	-----

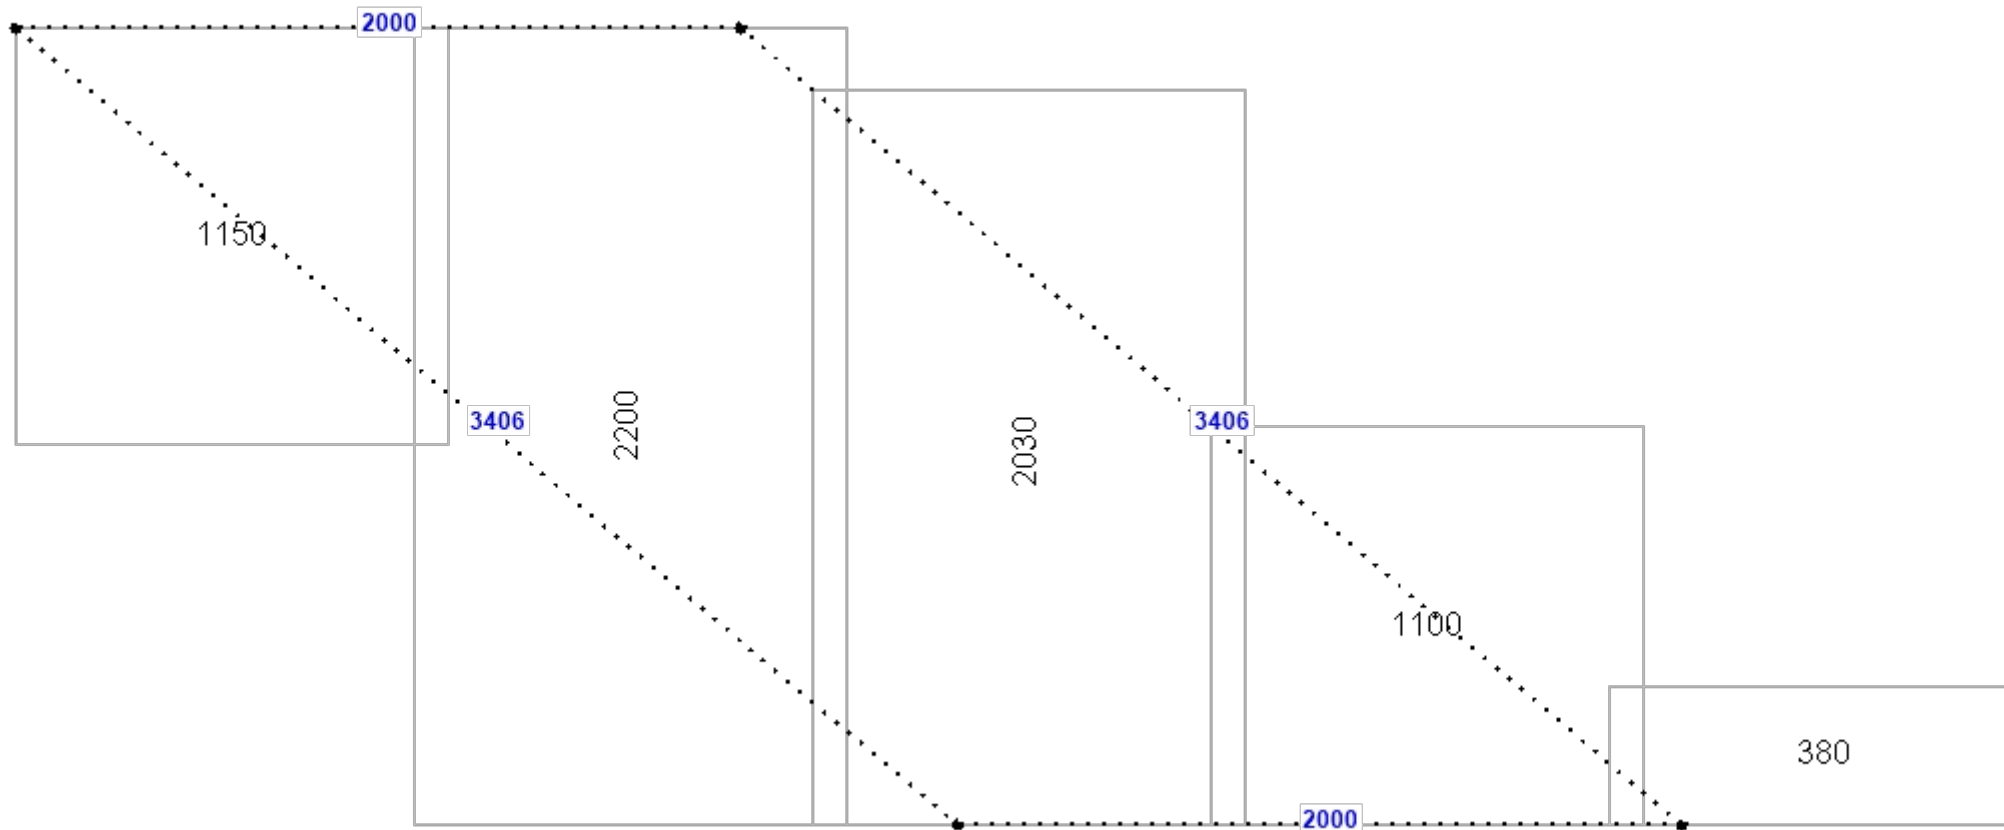


Length | Number of sheets | Area E | Area T

Szerelési útmutató

Tető	Ház 1	Felület	5,72m ² (Σ=200,32m ²)	Dőlésszöge
Felület	Udvar kiugró Konty	Körfogat	11,21m	

Anyag	BONA PLUS 2.0 350	Mennyiség	9,3 m ²	Udvar kiugró Konty	ΔX: 0	ΔY:
-------	-------------------	-----------	--------------------	--------------------	-------	-----

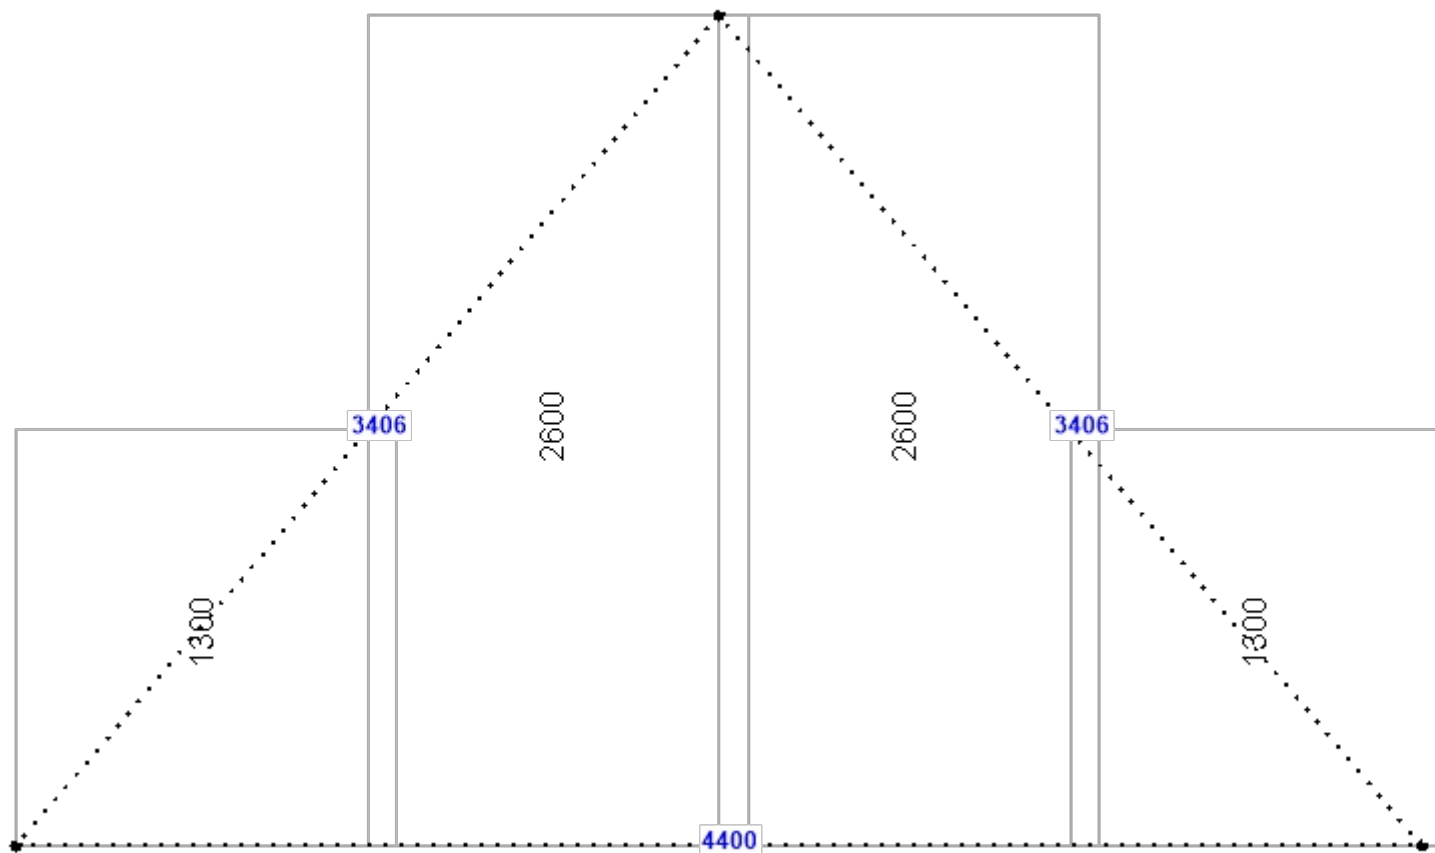


Length | Number of sheets | Area E | Area T

Szerelési útmutató


Tető	Ház 1	Felület	4,4m ² (Σ=200,32m ²)	Dőlésszöge
Felület	Udvar kiugró 2	Körfogat	10,81m	

Anyag	BONA PLUS 2.0 350	Mennyiség	7,87 m2	Udvar kiugró 2	ΔX: 0	ΔY:
-------	-------------------	-----------	---------	----------------	-------	-----

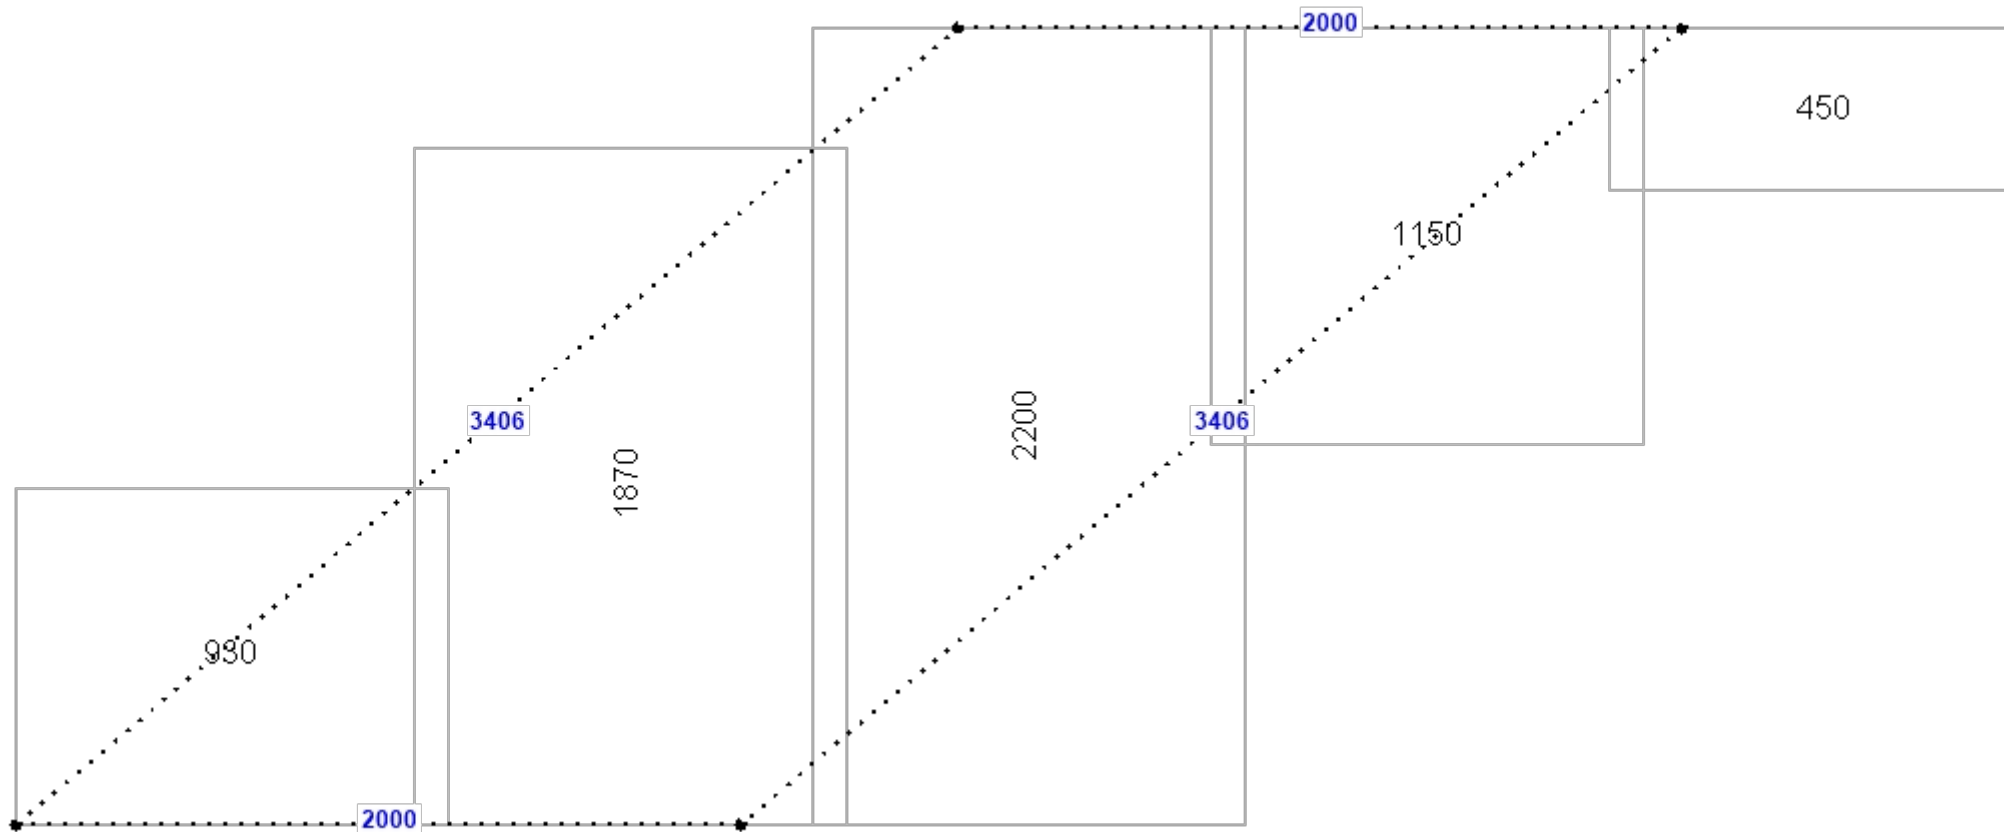


Length | Number of sheets | Area E | Area T

Szerelési útmutató						
Tető Felület	Ház 2 oldal 1	Felület Körfogat	26,19m ² (Σ=64,26m ²) 24,8m	Dőlésszöge	0,0	
Anyag	BONA PLUS 2.0 350	Mennyiség	28,97 m2	oldal 1	ΔX: 0	ΔY:

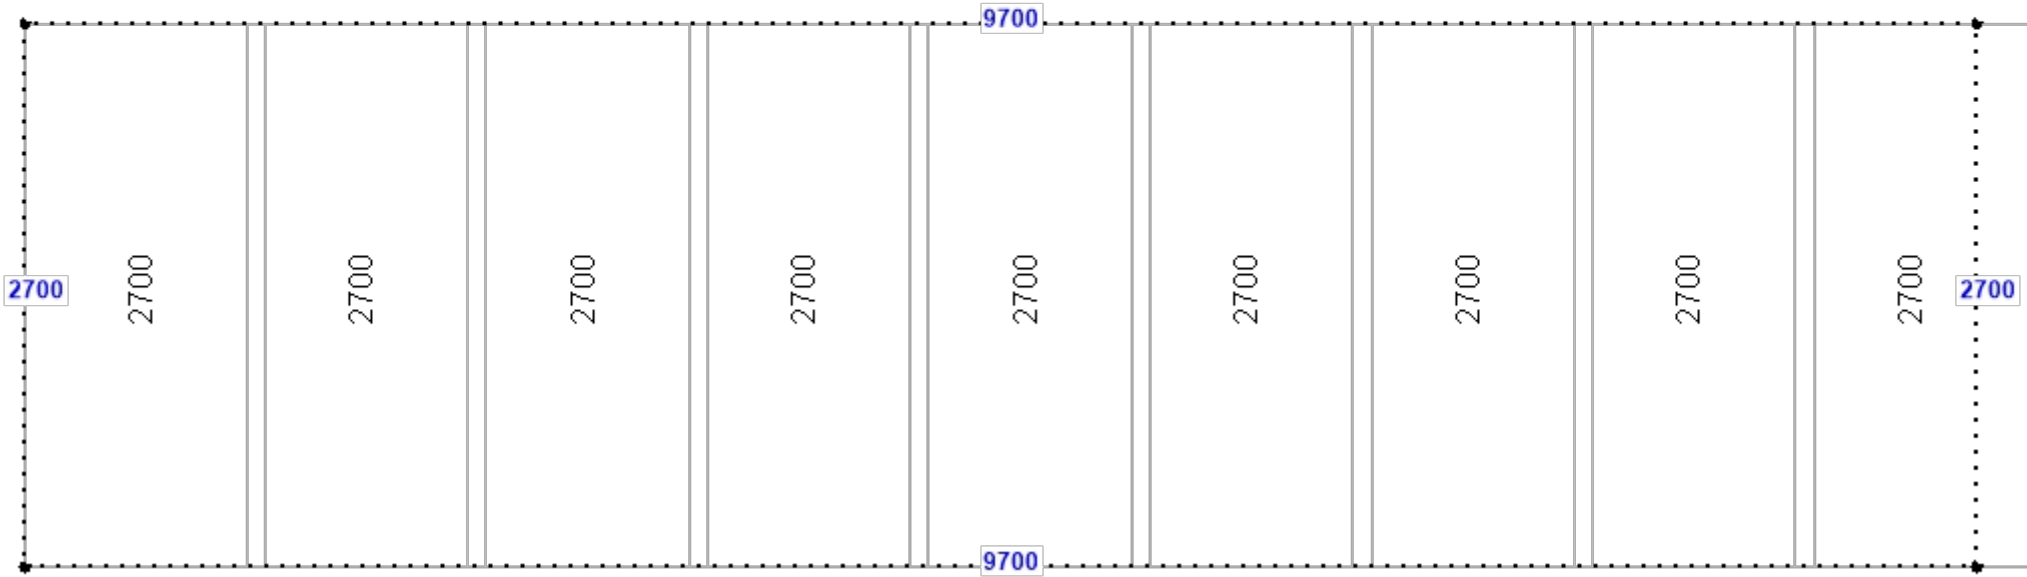

Length	Number of sheets	Area E	Area T
--------	------------------	--------	--------

Szerelési útmutató						
Tető Felület	Ház 2 oldal 2	Felület Körfogat	26,19m ² (Σ=64,26m ²) 24,8m	Dőlésszöge	0,0	
Anyag	BONA PLUS 2.0 350	Mennyiség	28,97 m2	oldal 2	ΔX: 0	ΔY:

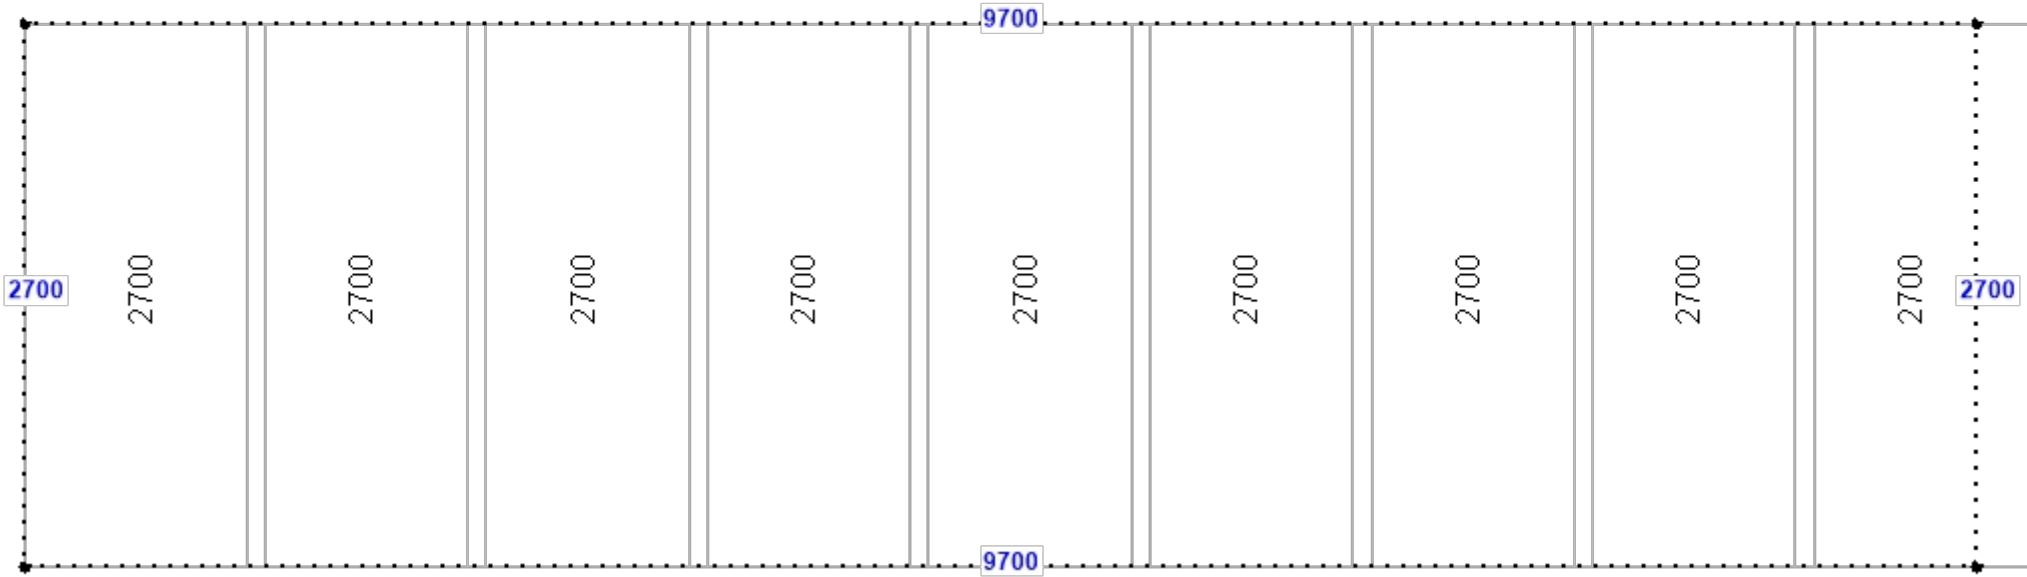


Length | Number of sheets | Area E | Area T

Szerelési útmutató

Tető	Ház 2	Felület	11,88m ² (Σ=64,26m ²)	Dőlésszöge
Felület	Előtető	Körfogat	13,8m	

Anyag	BONA PLUS 2.0 350	Mennyiség	12,87 m2	Előtető	ΔX: 0	ΔY:
-------	-------------------	-----------	----------	---------	-------	-----

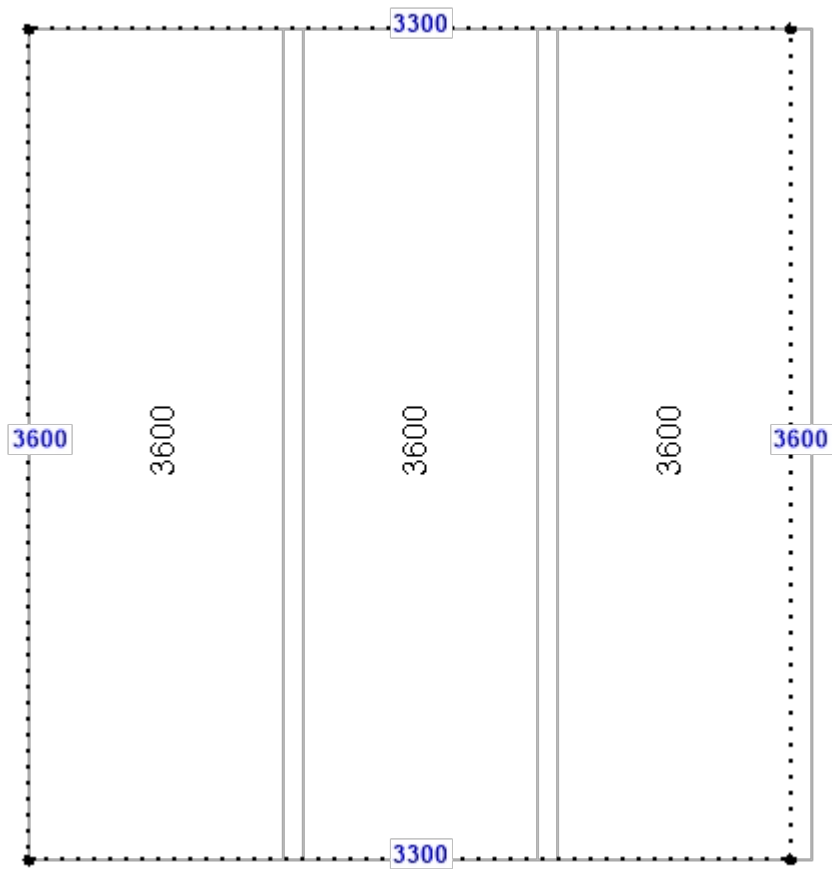


Length | Number of sheets | Area E | Area T

Szerelési útmutató

Tető	Ház 3	Felület	7,75m ² (Σ=68,62m ²)	Dőlésszöge	0,0
Felület	Konty 1	Körfogat	12,96m		

Anyag	BONA PLUS 2.0 350	Mennyiség	11,99 m2	Konty 1	ΔX: 250	ΔY:
-------	-------------------	-----------	----------	---------	---------	-----

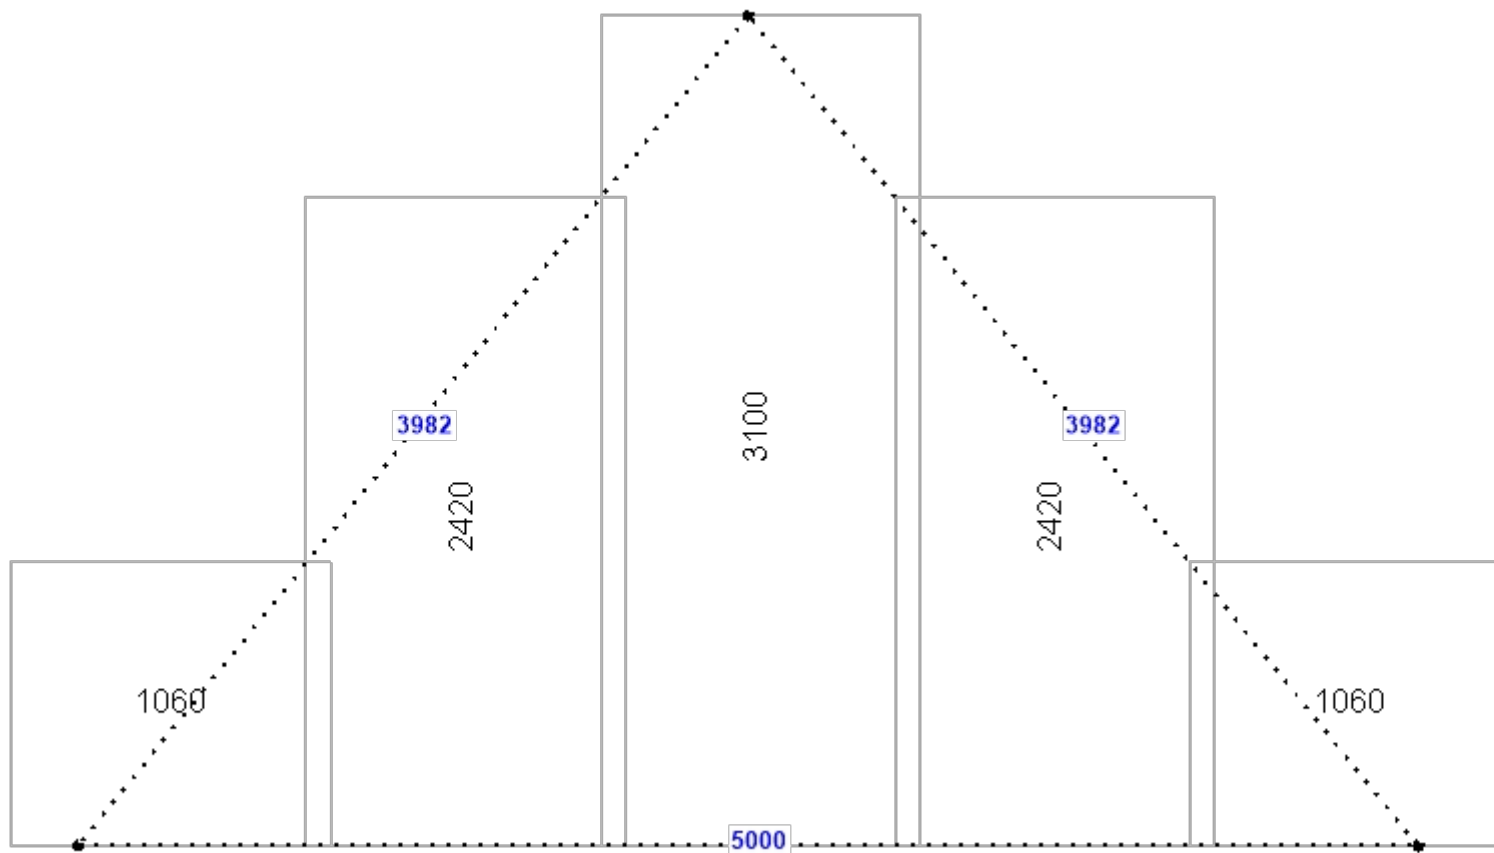


Length | Number of sheets | Area E | Area T

Szerelési útmutató

Tető	Ház 3	Felület	7,75m ² (Σ=68,62m ²)	Dőlésszöge	0,0
Felület	Konty 2	Körfogat	12,96m		

Anyag	BONA PLUS 2.0 350	Mennyiség	11,99 m2	Konty 2	ΔX: 250	ΔY:
-------	-------------------	-----------	----------	---------	---------	-----

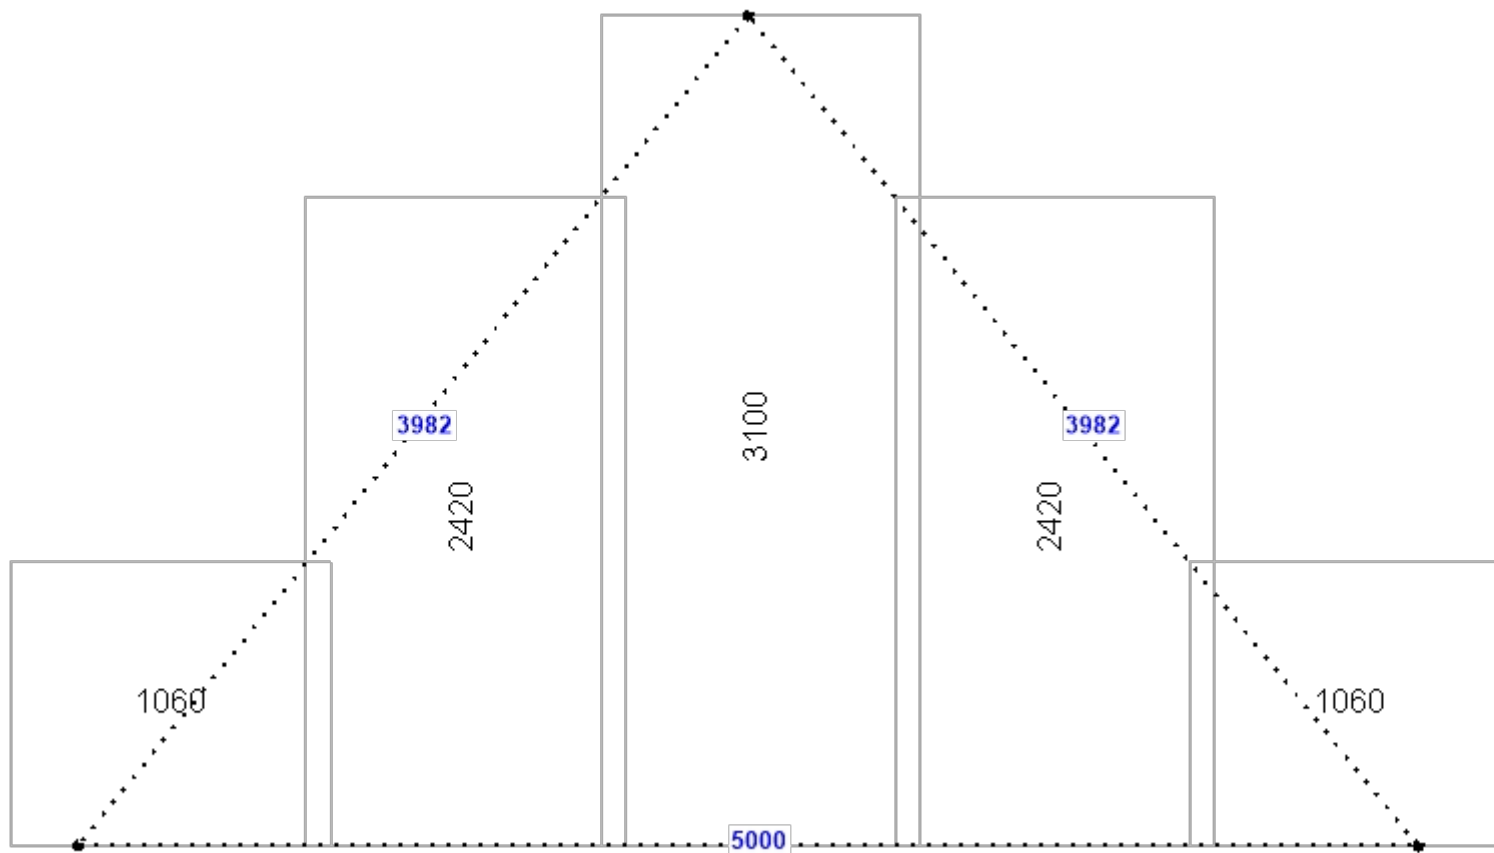


Length | Number of sheets | Area E | Area T

Szerelési útmutató

Tető	Ház 3	Felület	26,56m ² (Σ=68,62m ²)	Dőlésszöge
Felület	Oldal 1	Körfogat	24,85m	

Anyag	BONA PLUS 2.0 350	Mennyiség	32,29 m2	Oldal 1	ΔX: 0	ΔY:
-------	-------------------	-----------	----------	---------	-------	-----

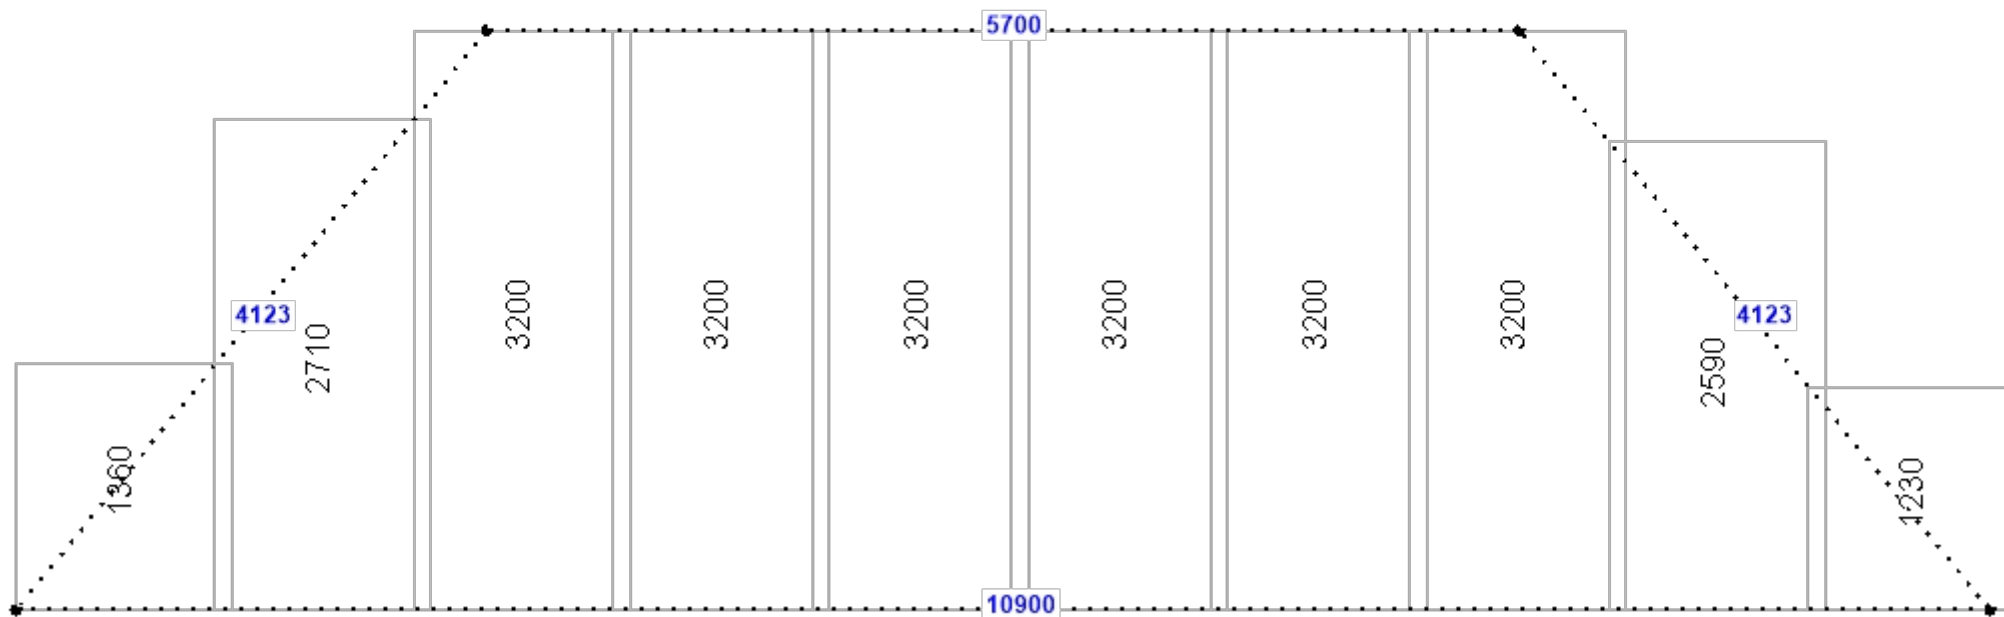


Length | Number of sheets | Area E | Area T

Szerelési útmutató

Tető	Ház 3	Felület	26,56m ² (Σ=68,62m ²)	Dőlésszöge
Felület	Oldal 2	Körfogat	24,85m	

Anyag	BONA PLUS 2.0 350	Mennyiség	32,29 m2	Oldal 2	ΔX: 0	ΔY:
-------	-------------------	-----------	----------	---------	-------	-----

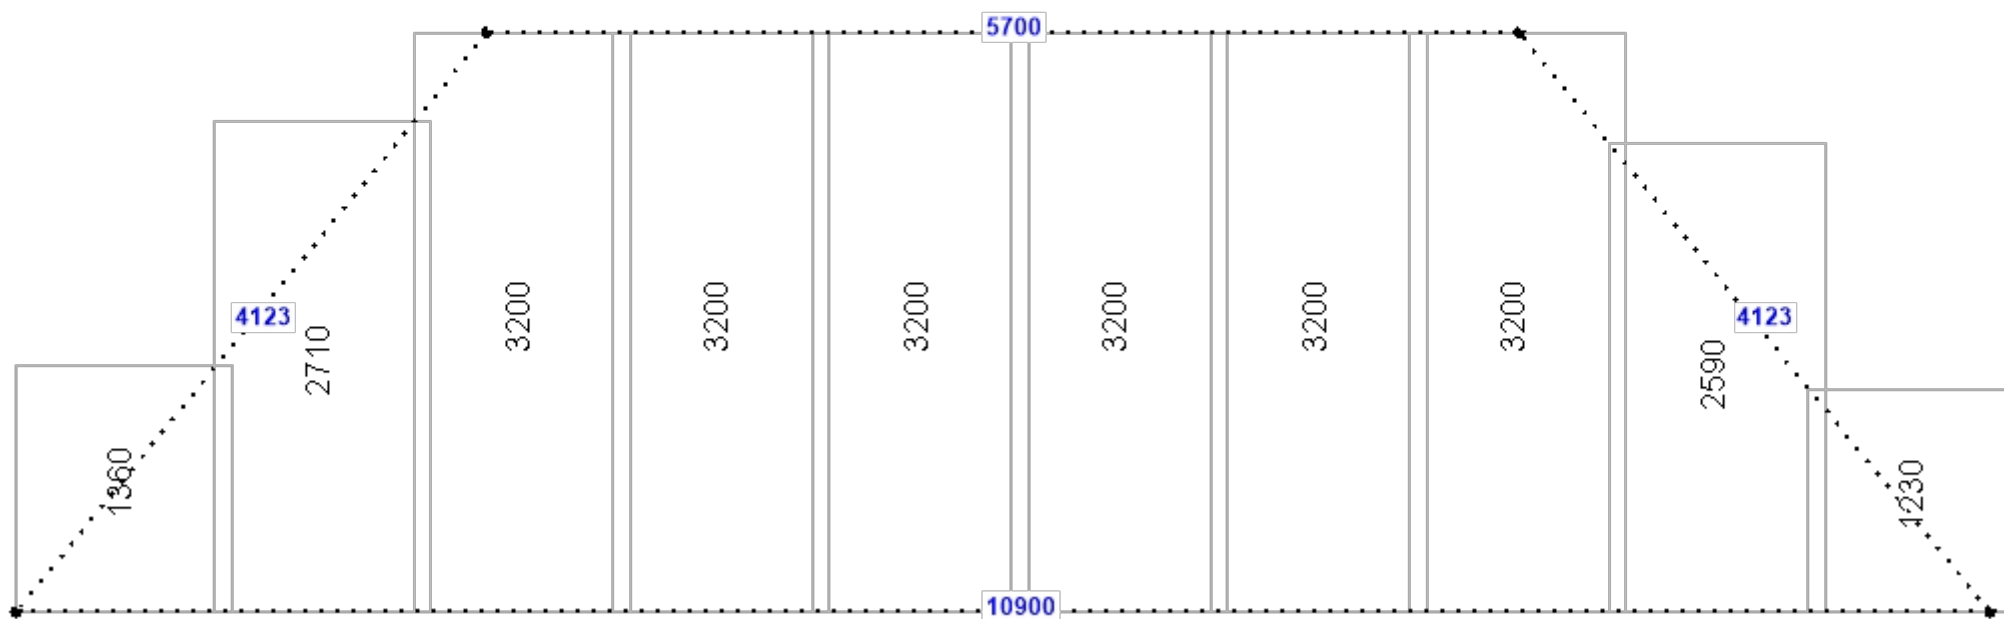

Length | Number of sheets | Area E | Area T